


POS 14

Supp lame dx e sx 2pz sp12

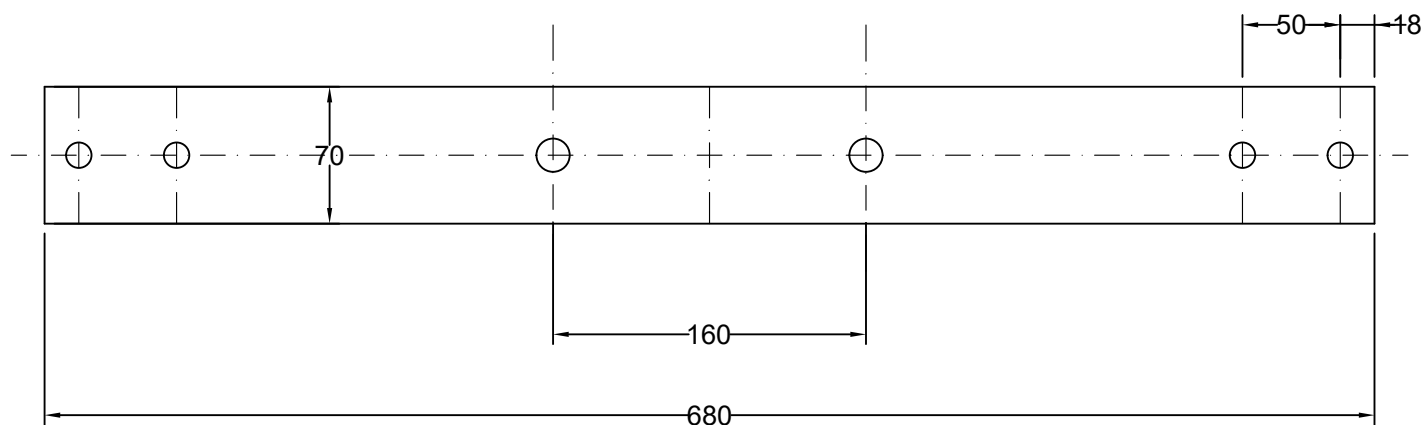

POS 16

Supp lama centrale 1pz sp12

